(PARVEEN KUMAR) SD(HQ) | (PRIYA SONI) ATP(HQ) | (BABITA GUPTA) DTP (HQ) | (VIJENDER SINGH) STP (HQ) | (BHUVNESH KUMAR) CTP(HR) | (AMIT KHATRI, IAS) DTCP (HR)

This is a "PROVISIONAL APPROVED LAYOUT PLAN"
Only for Purpose of inviting
Objection from the general public

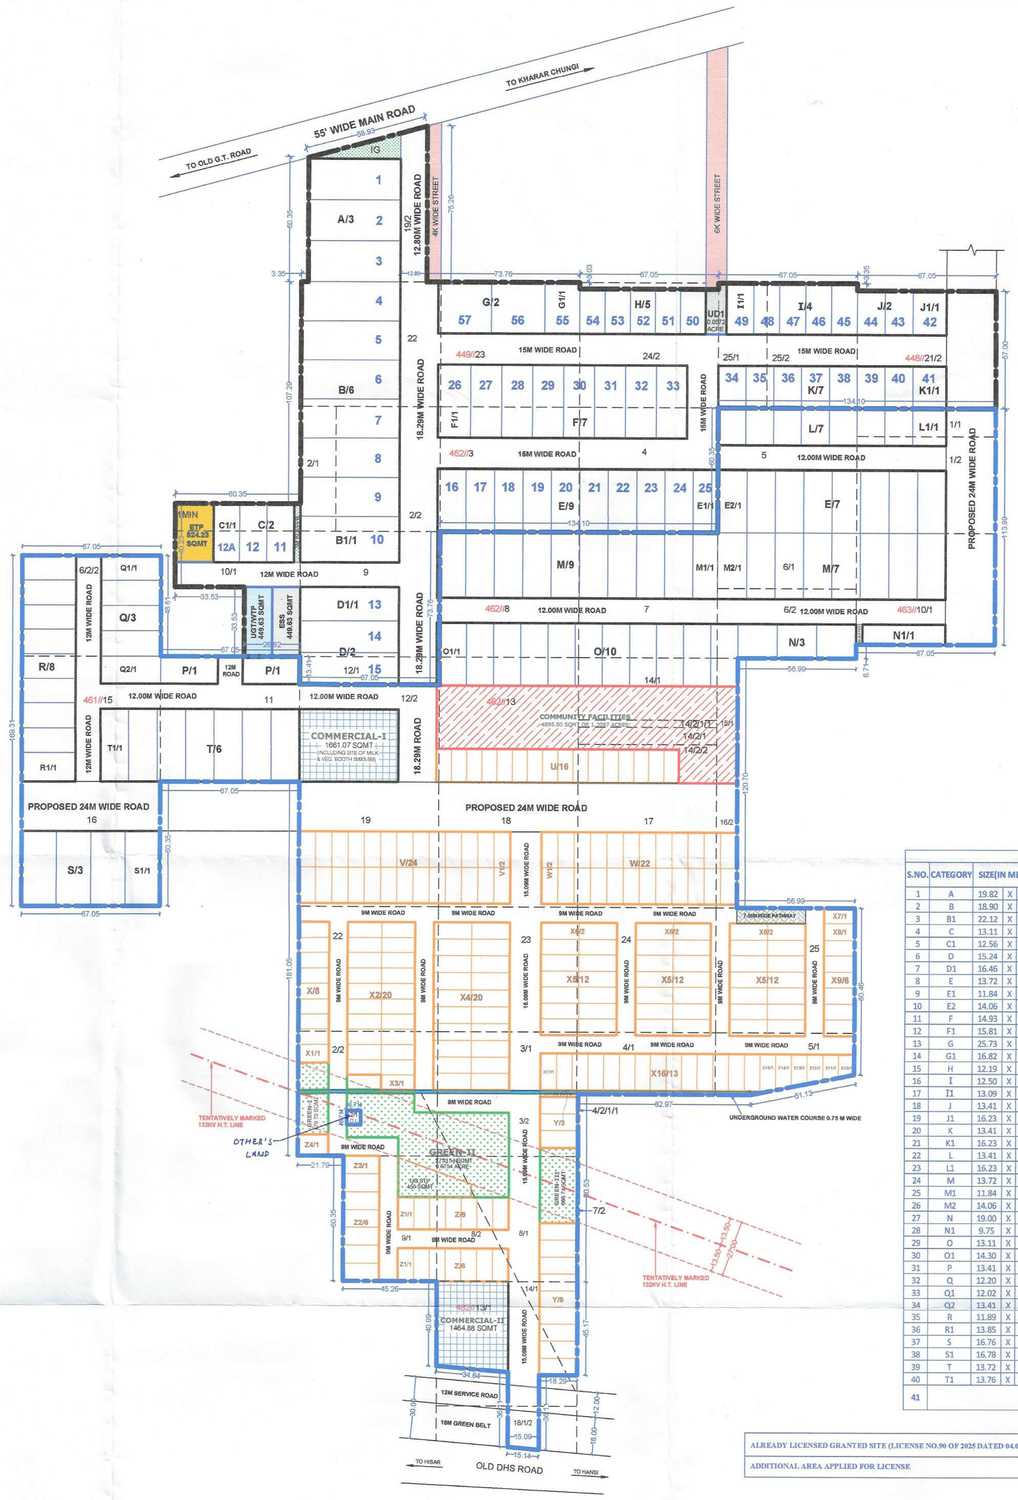

AREA CHART FOR RESIDENTIAL PLOTS UNDER DDJAY-2016			
S.NO.	PARTICULARS		
1.	**SALEABLE AREA/PLOTTED AREA**	7.2417 ACRES	
2.	GROSS SITE AREA	7.2417/61% = 11.8716 ACRES	
3.	REQUIRED AREA FOR PARK/GREEN	0.8903 ACRE	7.50%
4.	**PROPOSED AREA FOR PARK/GREEN**	0.9687 ACRE	8.08%
5.	REQUIRED COMMUNITY SITE	1.1871 ACRES	10.00%
6.	**PROVIDED COMMUNITY SITE**	1.2097 ACRES	10.19%

DENSITY CALCULATION(PPA):-
NUMBER OF RESIDENTIAL PLOTS = 220
UNITS ALLOWED = 4
POPULATION ALLOWED PER UNIT = 4.5
DENSITY CALCULATION = 220 X 4 X 4.5 = 3960.0 / 11.8716 = **333.57 PPA, SAY 334 PPA**
(PERMISSIBLE DENSITY: 240 PPA - 400 PPA)

GREEN AREA CALCULATION-
= GREEN-I + GREEN-II + GREEN-III
= 479.73 + 2733.54 + 666.74
= 3880.01 SQMT OR 0.9587 ACRE

DETAIL OF RESIDENTIAL PLOTS

S.NO.	CATEGORY	SIZE(IN METERS)				AREA(IN SQMT)	NO. OF PLOTS		TOTAL(IN SQMT)		
1	U	7.32	X	15.95	=	116.75	16	=	1868.00		
2	V	7.81	X	17.45	=	136.28	24	=	3270.72		
3	V1	7.85	X	17.45	=	136.98	2	=	273.96		
4	W	7.88	X	17.45	=	137.51	22	=	3025.22		
5	W1	7.89	X	17.45	=	137.68	2	=	275.36		
6	X	7.40	X	14.50	=	107.30	8	=	858.40		
7	X1	8.85	X	14.50	=	128.33	1	=	128.33		
8	X2	7.40	X	16.25	=	120.25	20	=	2405.00		
9	X3	7.30	X	16.25	=	118.63	1	=	118.63		
10	X4	8.13	X	18.29	=	148.70	20	=	2974.00		
11	X5	7.70	X	18.29	=	140.83	36	=	5069.88		
12	X6	7.97	X	18.29	=	145.77	6	=	874.62		
13	X7	7.55	X	14.82	=	111.89	1	=	111.89		
14	X8	7.97	X	14.82	=	118.12	1	=	118.12		
15	X9	7.70	X	14.82	=	114.11	6	=	684.66		
16	X10	AS PER PLAN			=	79.52	1	=	79.52		
17	X11	AS PER PLAN			=	90.98	1	=	90.98		
18	X12	AS PER PLAN			=	102.44	1	=	102.44		
19	X13	AS PER PLAN			=	113.89	1	=	113.89		
20	X14	AS PER PLAN			=	125.35	1	=	125.35		
21	X15	AS PER PLAN			=	135.57	1	=	135.57		
22	X16	7.57	X	18.13	=	137.24	13	=	1784.12		
23	X17	7.73	X	18.13	=	140.14	1	=	140.14		
24	Y	8.16	X	18.29	=	149.25	12	=	1791.00		
25	Z	7.62	X	15.80	=	120.40	12	=	1444.80		
26	Z1	7.68	X	15.80	=	121.34	2	=	242.68		
27	Z2	8.62	X	17.38	=	149.82	6	=	898.92		
28	Z3	8.63	X	17.38	=	149.99	1	=	149.99		
29	Z4	10.34	X	14.50	=	149.93	1	=	149.93		
30							**220**	=	29306.12	SQMT	
									7.2417	ACRES	20.08%

DETAIL OF INDUSTRIAL PLOTS

S.NO.	CATEGORY	SIZE(IN METERS)				AREA(IN SQMT)	NO. OF PLOTS		TOTAL(IN SQMT)	
1	A	19.82	X	44.19	=	875.85	3	=	2627.55	
2	B	18.90	X	47.54	=	898.51	6	=	5391.06	
3	B1	22.12	X	47.54	=	1051.58	1	=	1051.58	
4	C	13.11	X	28.23	=	370.10	2	=	740.20	
5	C1	12.56	X	28.23	=	354.57	1	=	354.57	
6	D	15.24	X	47.54	=	724.51	2	=	1449.02	
7	D1	16.46	X	47.54	=	782.51	1	=	782.51	
8	E	13.72	X	30.48	=	418.19	16	=	6691.04	
9	E1	11.84	X	30.48	=	360.88	1	=	360.88	
10	E2	14.06	X	30.48	=	428.55	1	=	428.55	
11	F	14.93	X	35.36	=	527.92	7	=	3695.44	
12	F1	15.81	X	35.36	=	559.04	1	=	559.04	
13	G	25.73	X	24.86	=	639.65	2	=	1279.30	
14	G1	16.82	X	24.86	=	418.15	1	=	418.15	
15	H	12.19	X	21.83	=	266.11	5	=	1330.55	
16	I	12.50	X	24.86	=	310.75	4	=	1243.00	
17	I1	13.09	X	24.86	=	325.42	1	=	325.42	
18	J	13.41	X	21.51	=	288.45	2	=	576.90	
19	J1	16.23	X	21.51	=	349.11	1	=	349.11	
20	K	13.41	X	20.49	=	274.77	7	=	1923.39	
21	K1	16.23	X	20.49	=	332.55	1	=	332.55	
22	L	13.41	X	17.87	=	239.64	7	=	1677.48	
23	L1	16.23	X	17.87	=	290.03	1	=	290.03	
24	M	13.72	X	31.89	=	437.53	16	=	7000.48	
25	M1	11.84	X	31.89	=	377.58	1	=	377.58	
26	M2	14.06	X	31.89	=	448.37	1	=	448.37	
27	N	19.00	X	16.46	=	312.74	3	=	938.22	
28	N1	9.75	X	40.03	=	390.29	1	=	390.29	
29	O	13.11	X	30.29	=	397.10	10	=	3971.00	
30	O1	14.30	X	30.29	=	433.15	1	=	433.15	
31	P	13.41	X	27.525	=	369.11	2	=	738.22	
32	Q	12.20	X	29.025	=	354.11	3	=	1062.33	
33	Q1	12.02	X	29.025	=	348.88	1	=	348.88	
34	Q2	13.41	X	29.025	=	389.23	1	=	389.23	
35	R	11.89	X	26.025	=	309.44	8	=	2475.52	
36	R1	13.85	X	26.025	=	360.45	1	=	360.45	
37	S	16.76	X	36.35	=	609.23	3	=	1827.69	
38	S1	16.78	X	36.35	=	609.95	1	=	609.95	
39	T	13.72	X	34.94	=	479.38	6	=	2876.28	
40	T1	13.76	X	34.94	=	480.77	1	=	480.77	
41							**134**	=	58605.73	SQMT
									14.4818	ACRES 40.16%

ALREADY LICENSED GRANTED SITE (LICENSE NO.90 OF 2025 DATED 04.06.2025)	10.9125 ACRES
ADDITIONAL AREA APPLIED FOR LICENSE	25.26041 ACRES

PROPOSED COMBINED LAYOUT PLAN OF ADDITIONAL AREA(25.26041 ACRES) IN ALREADY LICENSED INDUSTRIAL PLOTTED COLONY OVER AN AREA MEASURING 10.9125 ACRES HAVING LICENCE NO.90 OF 2025 DATED 04.06.2025, THEREFORE TOTALLING 36.17291 ACRES, FALLING IN THE REVENUE ESTATE OF VILL. HANSI, SECTOR-18, TEH. HANSI & DISTT. HISAR, HARYANA, BEING DEVELOPED BY M/s. V.S. INFRATECH

AREA CALCULATIONS

S.NO.	PARTICULARS	PROPOSAL (ACRE)	PROPOSAL (%)	PERMISSIBLE (ACRE)	PERMISSIBLE (%)
1	ALREADY LICENSED AREA VIDE LICENCE NO.90 OF 2025 DATED 04.06.2025	10.9125	-	-	-
2	ADDITIONAL AREA APPLIED FOR LICENSE	25.26041	-	-	-
3	**TOTAL AREA OF THE SCHEME**	**36.17291**	-	-	-
4	AREA UNDER UD	0.0572	-	-	-
5	BALANCE AREA	36.11571	-	-	-
6	AREA UNDER 30M WIDE GREEN BELT INCLUDING 12M WIDE SERVICE ROAD	0.1122	-	-	-
7	BALANCE AREA	36.00351	-	-	-
8	50% BENEFIT OF AREA UNDER 30M WIDE GREEN BELT INCLUDING 12M WIDE SERVICE ROAD	0.0561	-	-	-
9	**NET PLANNED AREA**	**36.05961**	-	-	-
10	AREA UNDER RESIDENTIAL PLOTS (DDJAY)	7.2417	20.08%	9.0149	25%(MAXIMUM)
11	AREA UNDER COMMERCIAL	0.7724	2.14%		
12	AREA UNDER INDUSTRIAL PLOTS	14.4818	40.16%	14.4238	40%(MINIMUM)
13	**TOTAL SALEABLE AREA(10 + 11 + 12)**	**22.4959**	**62.39%**	**23.4387**	**65%(MAXIMUM)**
14	GREEN AREA / OPEN SPACE/ I.G. / ROADS / SERVICES / COMMUNITY FACILITIES	13.5637	37.61%	12.6208	35%(MINIMUM)

DIVINE
ARCHITECTS & PLANNERS
ADDRESS : SCO 76-77,1st FLOOR, SECTOR-8C, MADHYA MARG,CHANDIGARH-160009.
CONTACT : +91-98139-00375, +91-172-4785520
EMAIL : divinearchitects16@gmail.com

LEGEND:
ESS
PARKS/OPEN SPACES/IG
KILLA LINE
SCHEME BOUNDARY
REVENUE RASTA
UGT
ETP
COMMUNITY FACILITIES
WATER COURSE
COMMERCIAL
UG STP

RESIDENTIAL PLOTS
INDUSTRIAL PLOTS

ABBREVIATIONS-
ESS = ELECTRIC SUB STATION
UGT = UNDERGROUND WATER TANK
WTP = WATER TREATMENT PLANT
ETP = EFFLUENT TREATMENT PLANT
UG STP = UNDERGROUND SEWAGE TREATMENT PLANT
IG = INCIDENTAL GREEN
O.L. = OTHER'S LAND

(SCALE-N.T.S.)

TOTAL COMMERCIAL AREA-
= COMMERCIAL-I + COMMERCIAL-II
= 1661.07 + 1464.88
= 3125.95 SQMT OR 0.7724 ACRE

NORTH
WEST EAST
SOUTH

For V.S. Infratech
Partner
SIGNATURE OF OWNER / APPLICANT

SCO 76-77, 1st Floor, Sector-8C, Chandigarh
AR. MONU SHARMA
CA/2018/78557
(M) 98139-00375
SIGNATURE OF ARCHITECT / TOWN PLANNER